


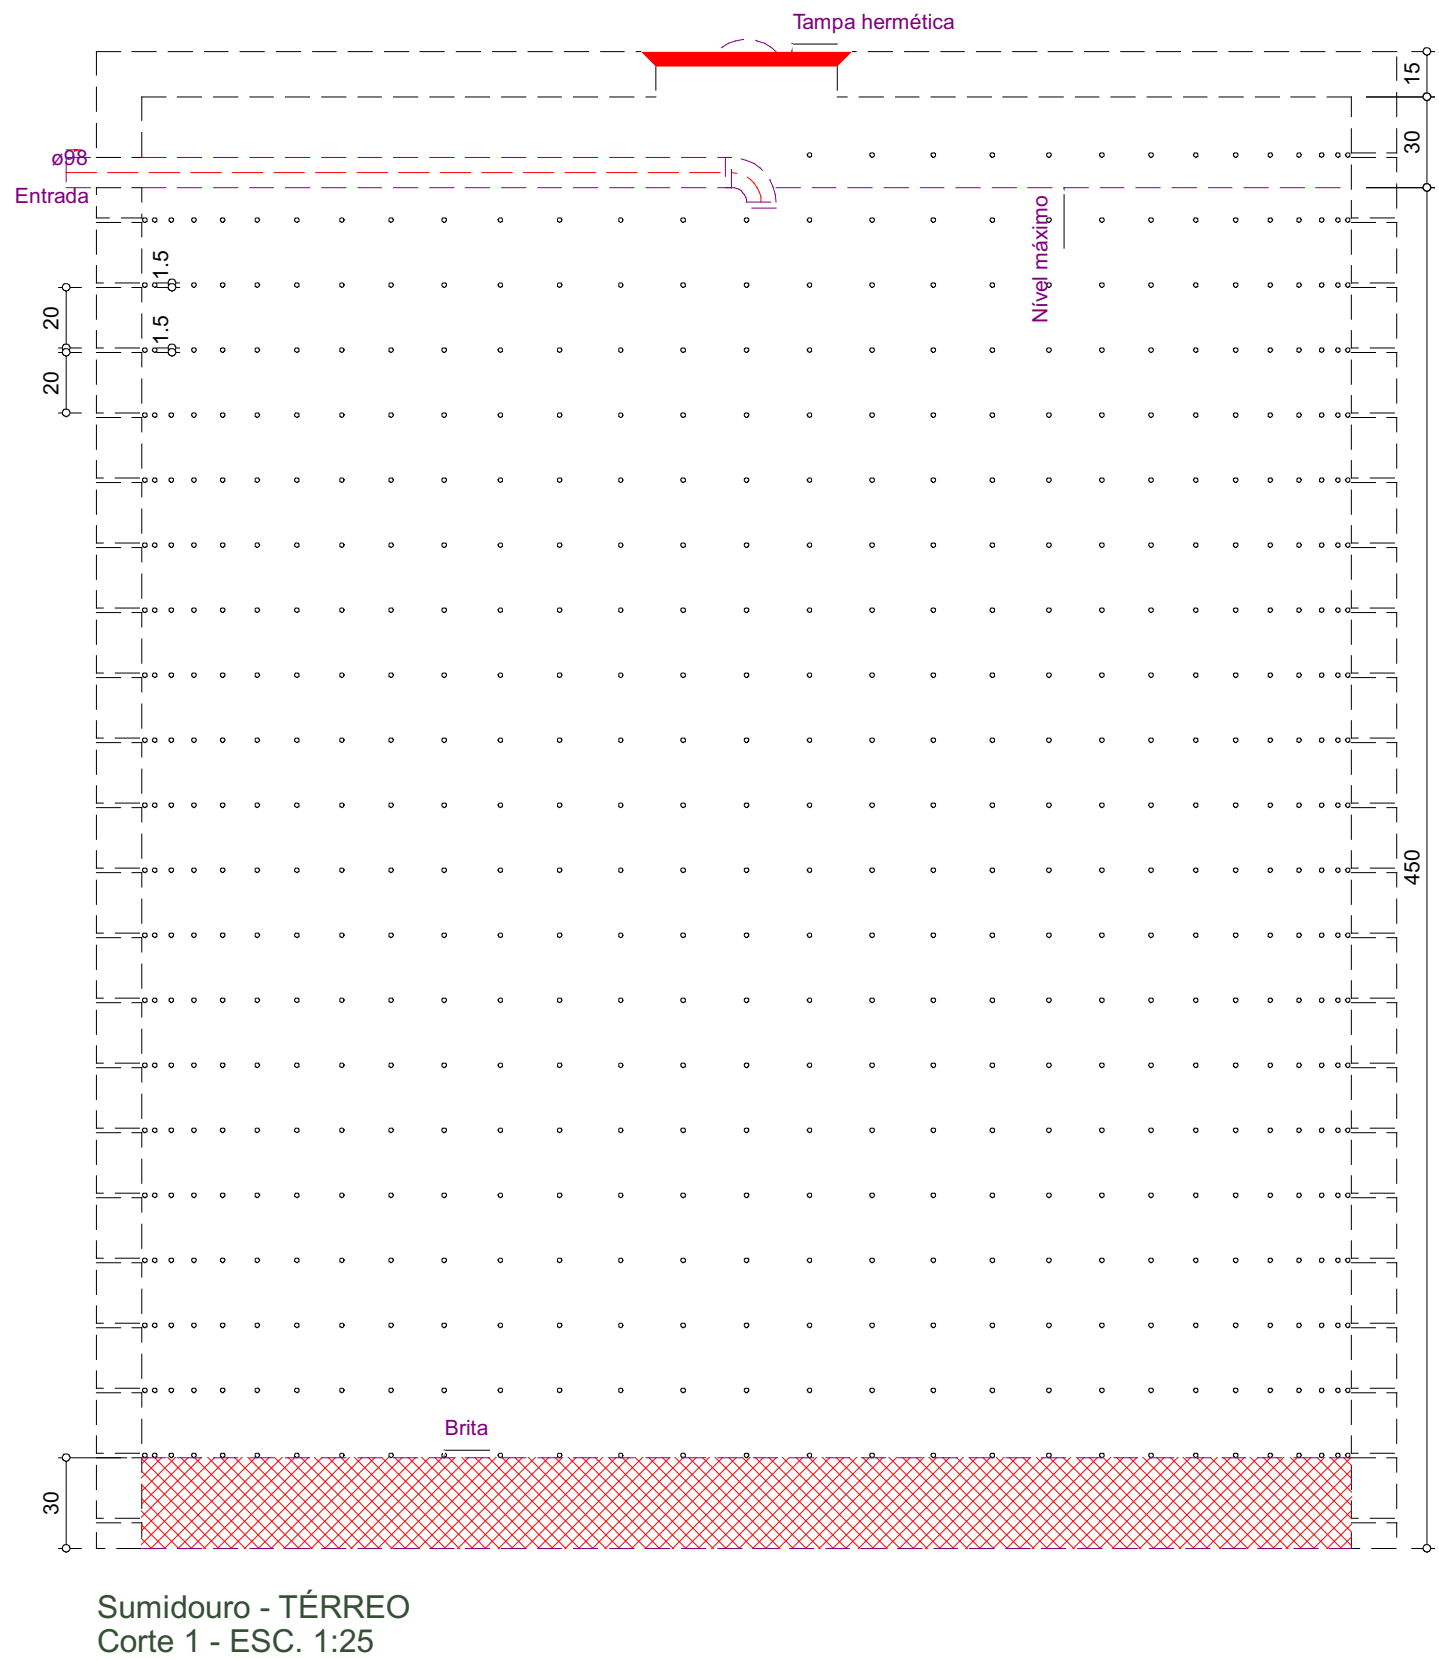
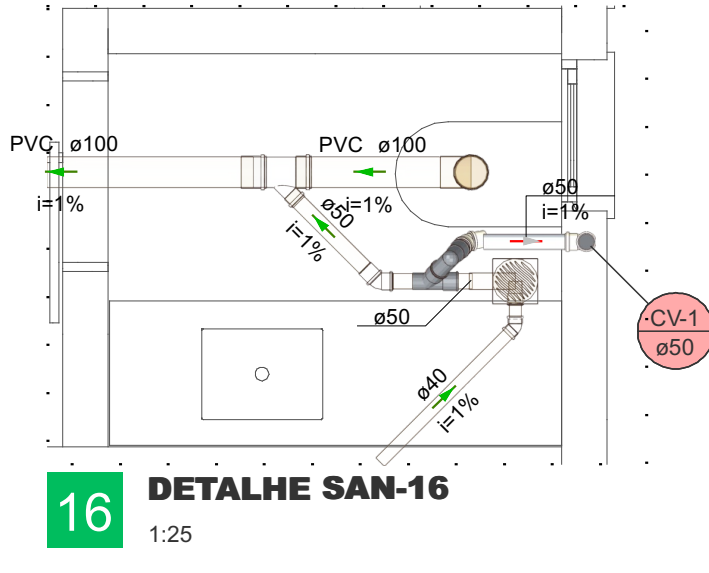
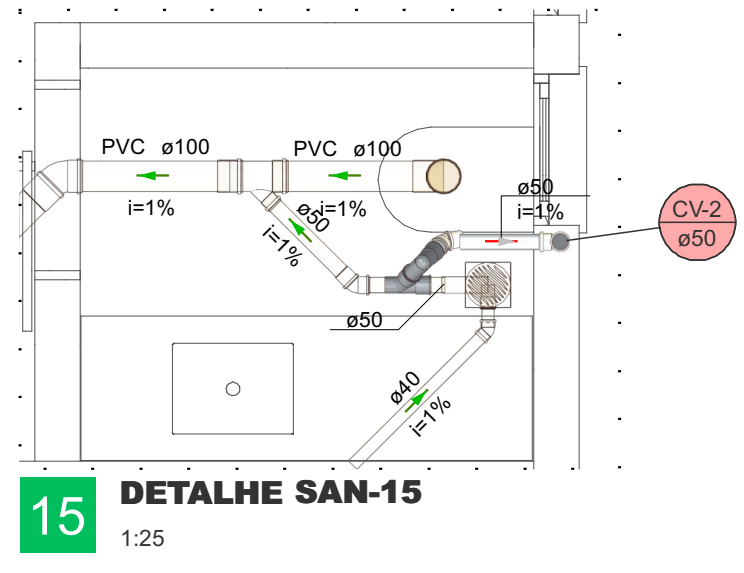
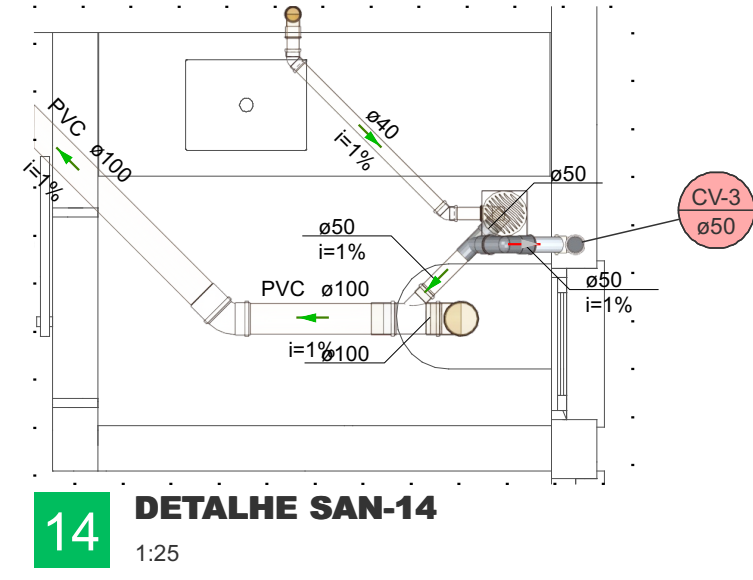
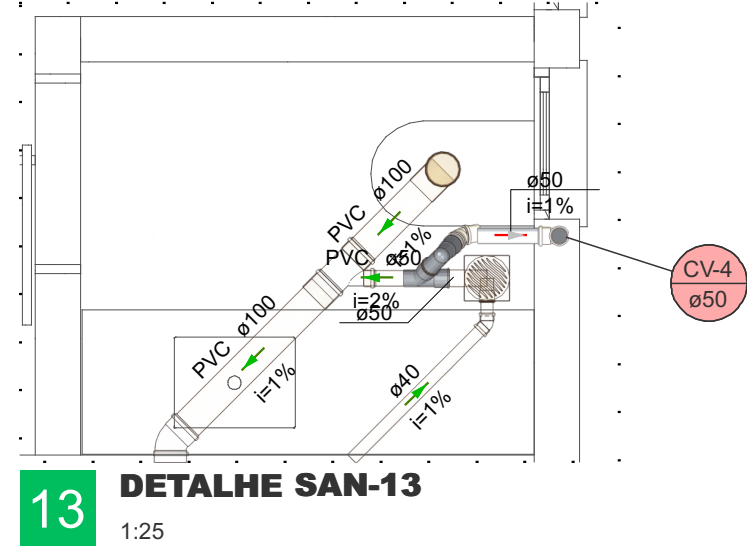
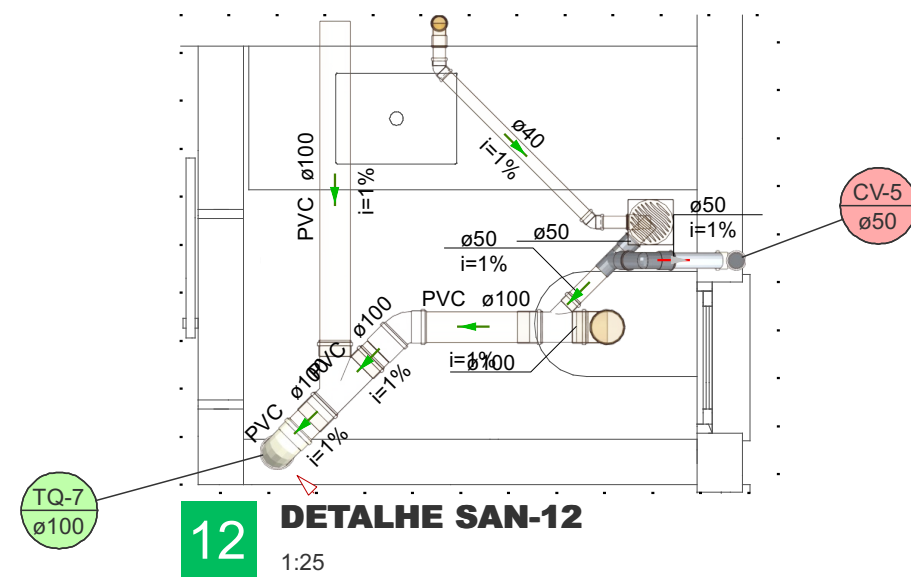
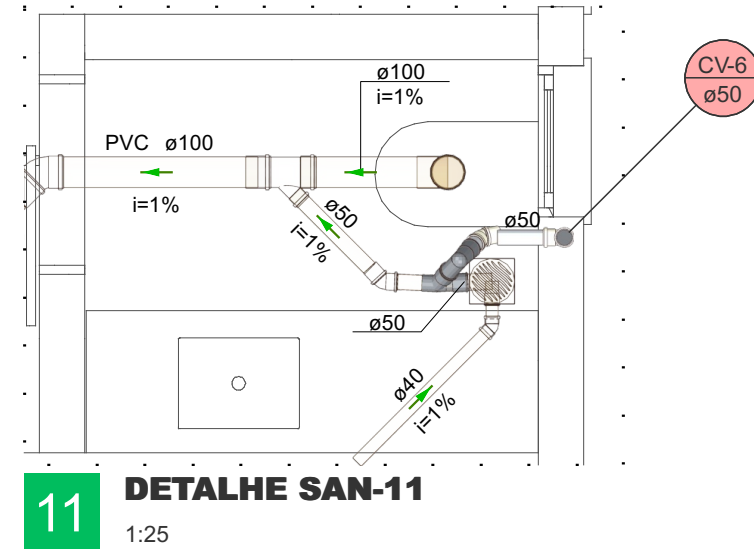
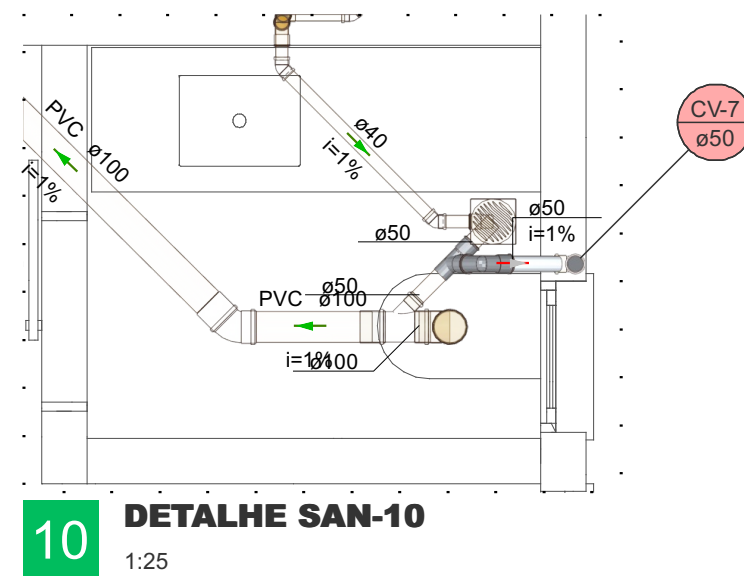
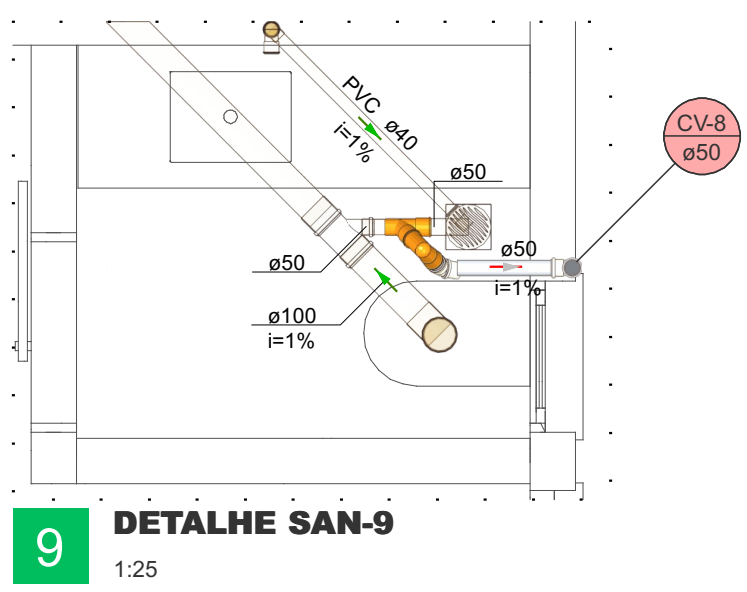
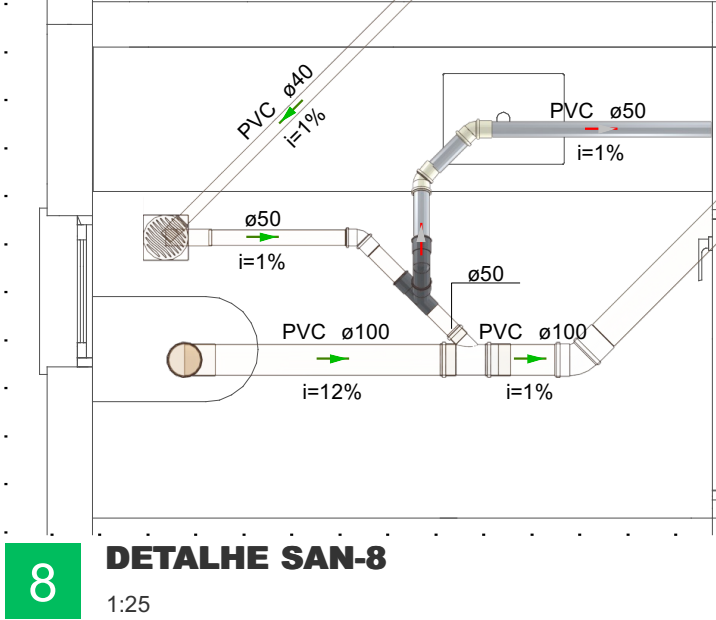
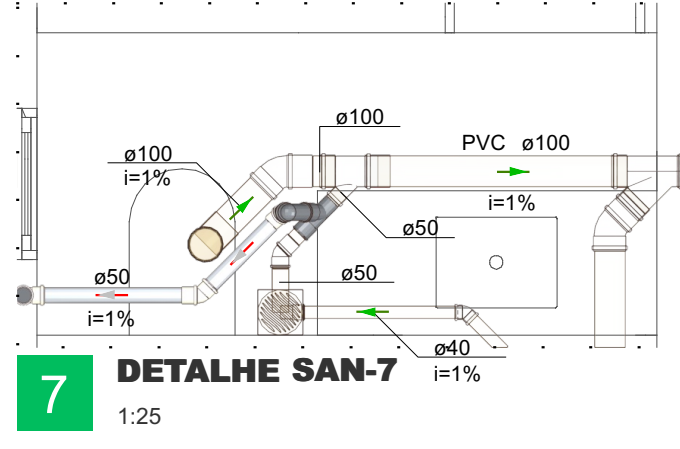
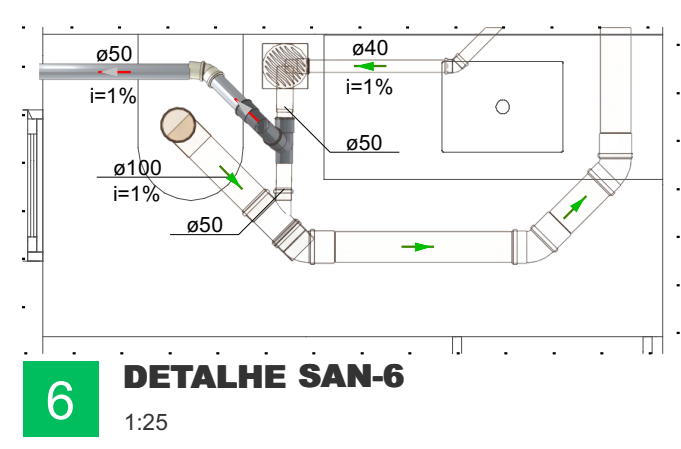
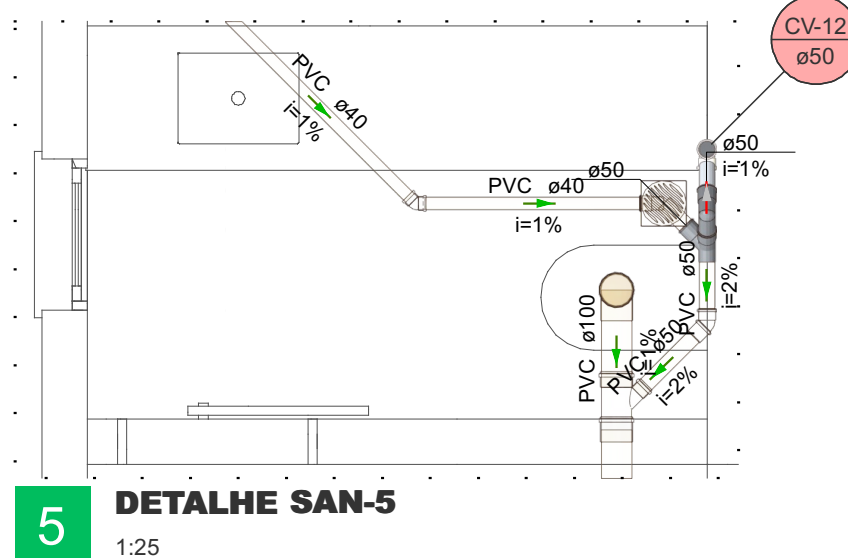
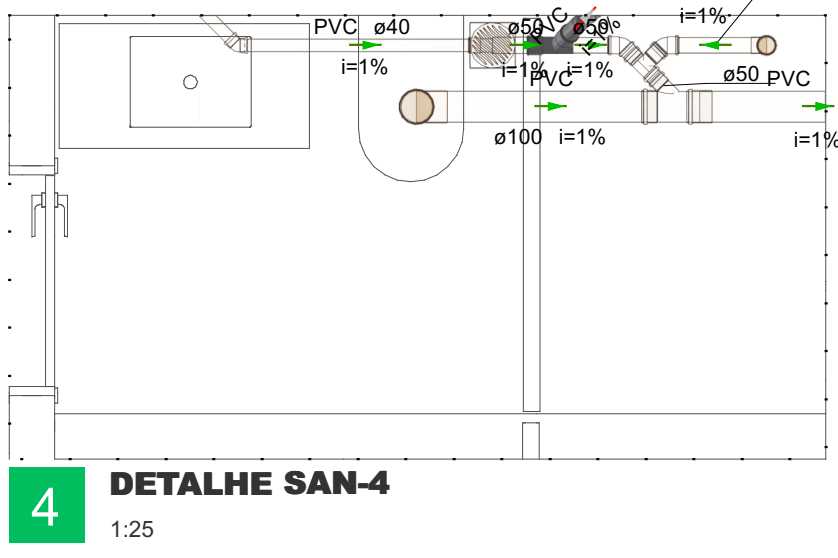
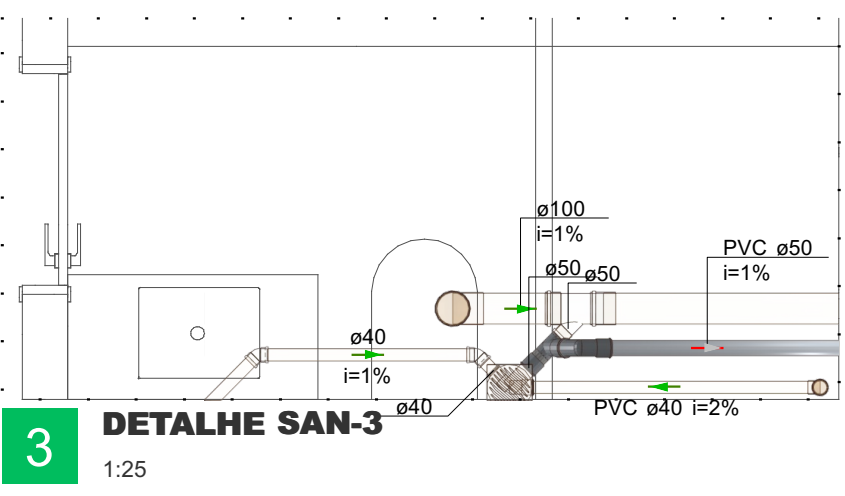
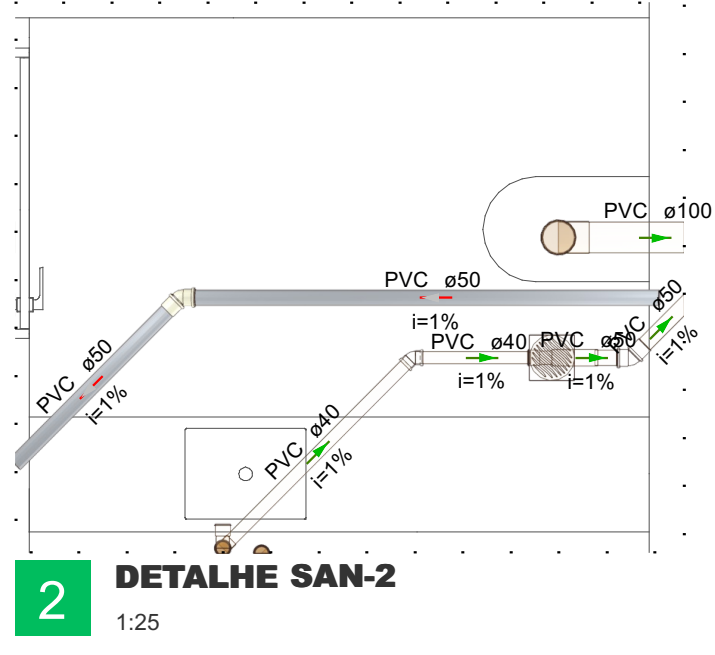


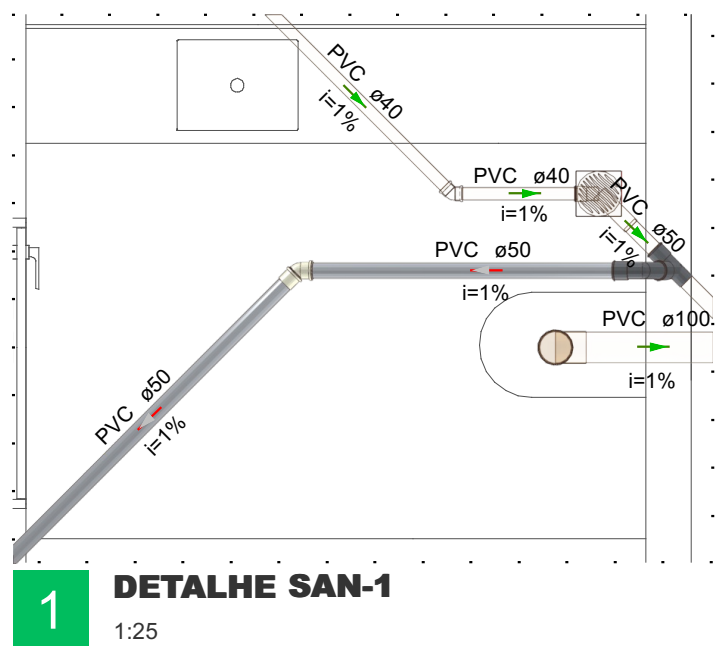


Sumidouro - TÉRREO
Corte 1 - ESC. 1:25

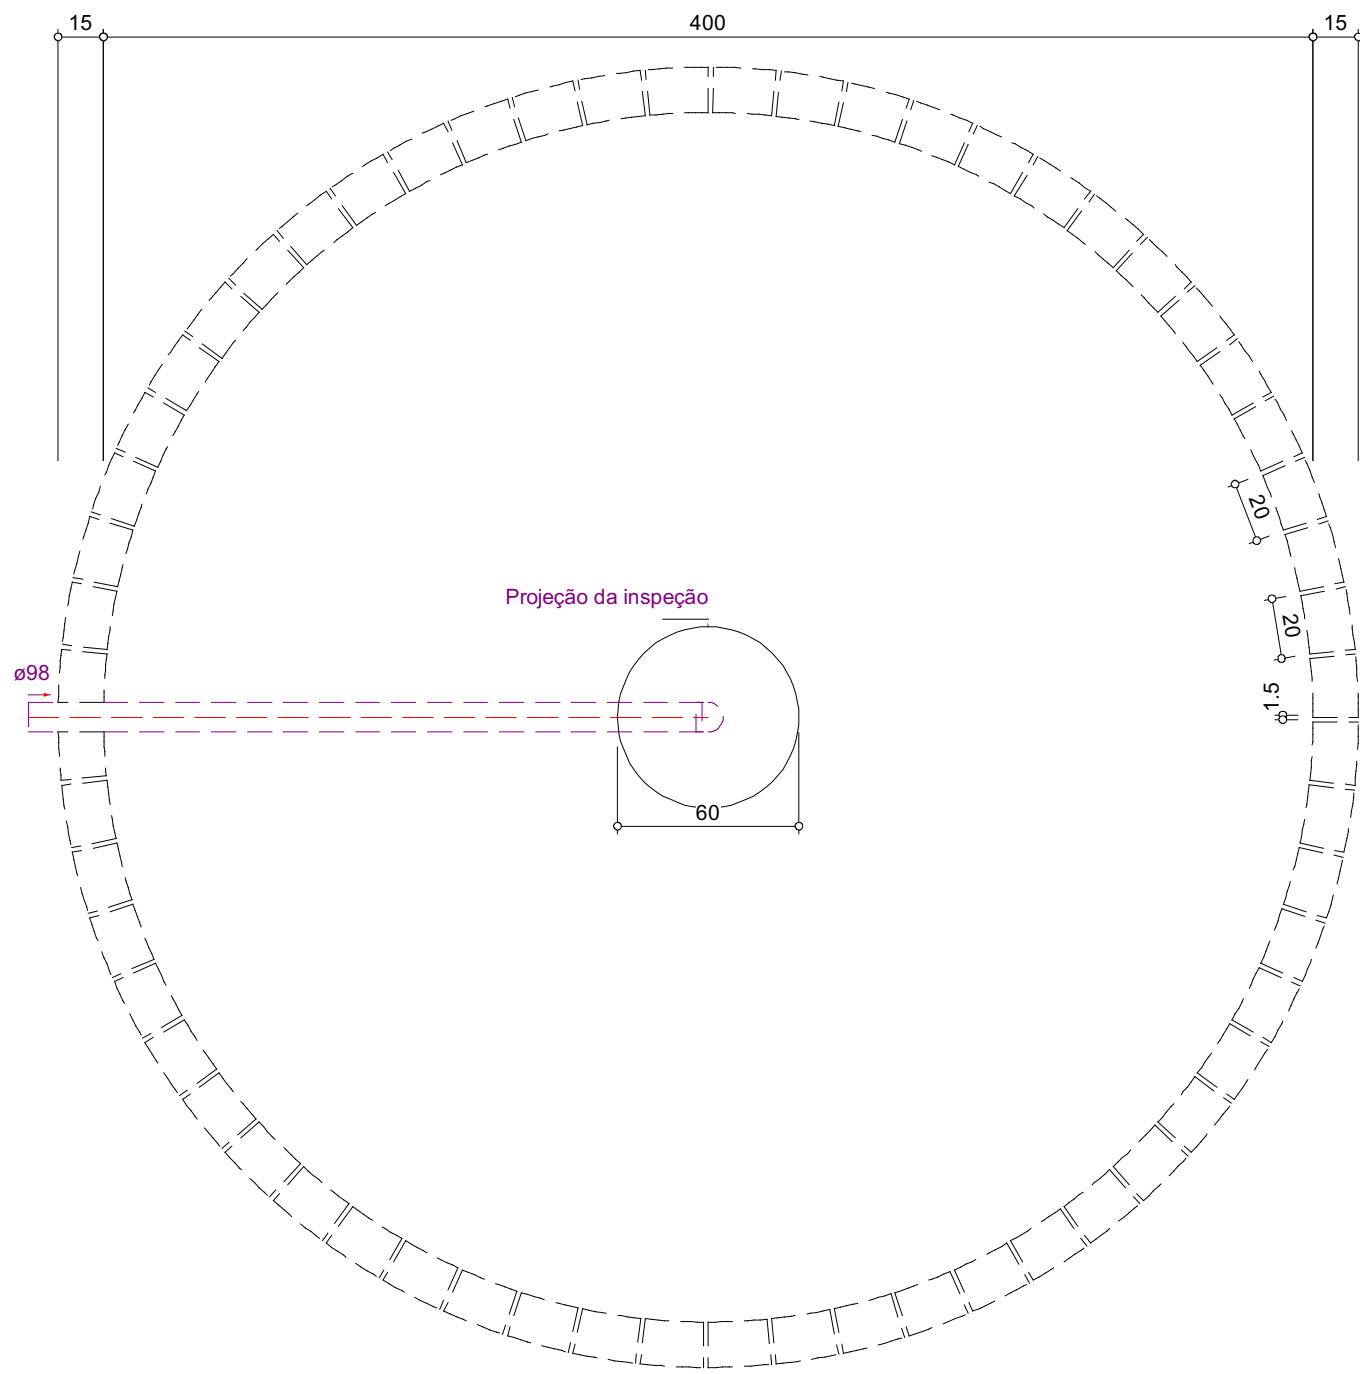

Sumidouro - TÉRREO
Planta baixa - ESC. 1:25

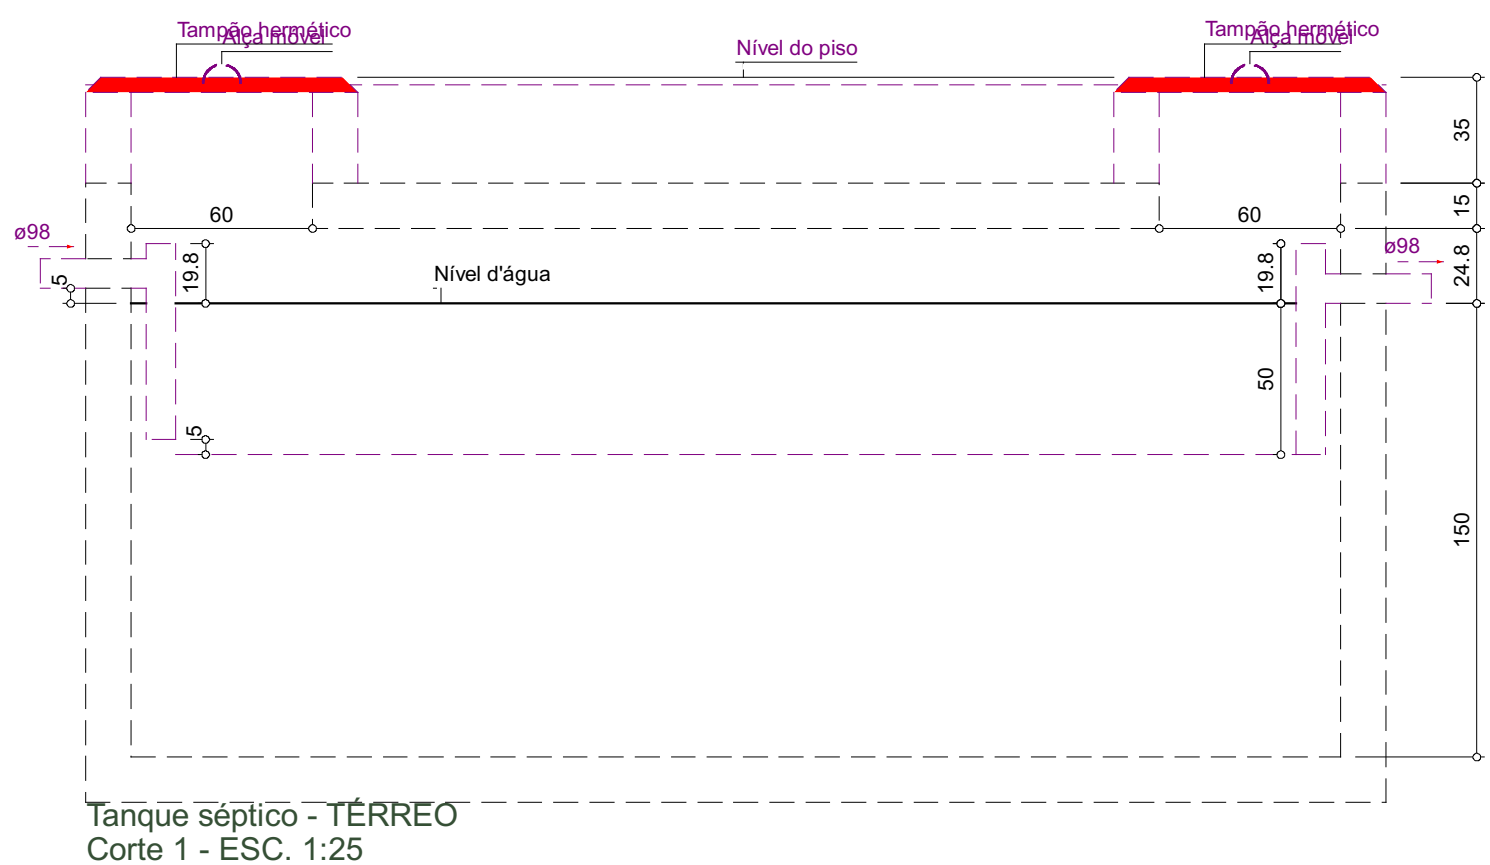

Tanque séptico - TÉRREO
Corte 1 - ESC. 1:25

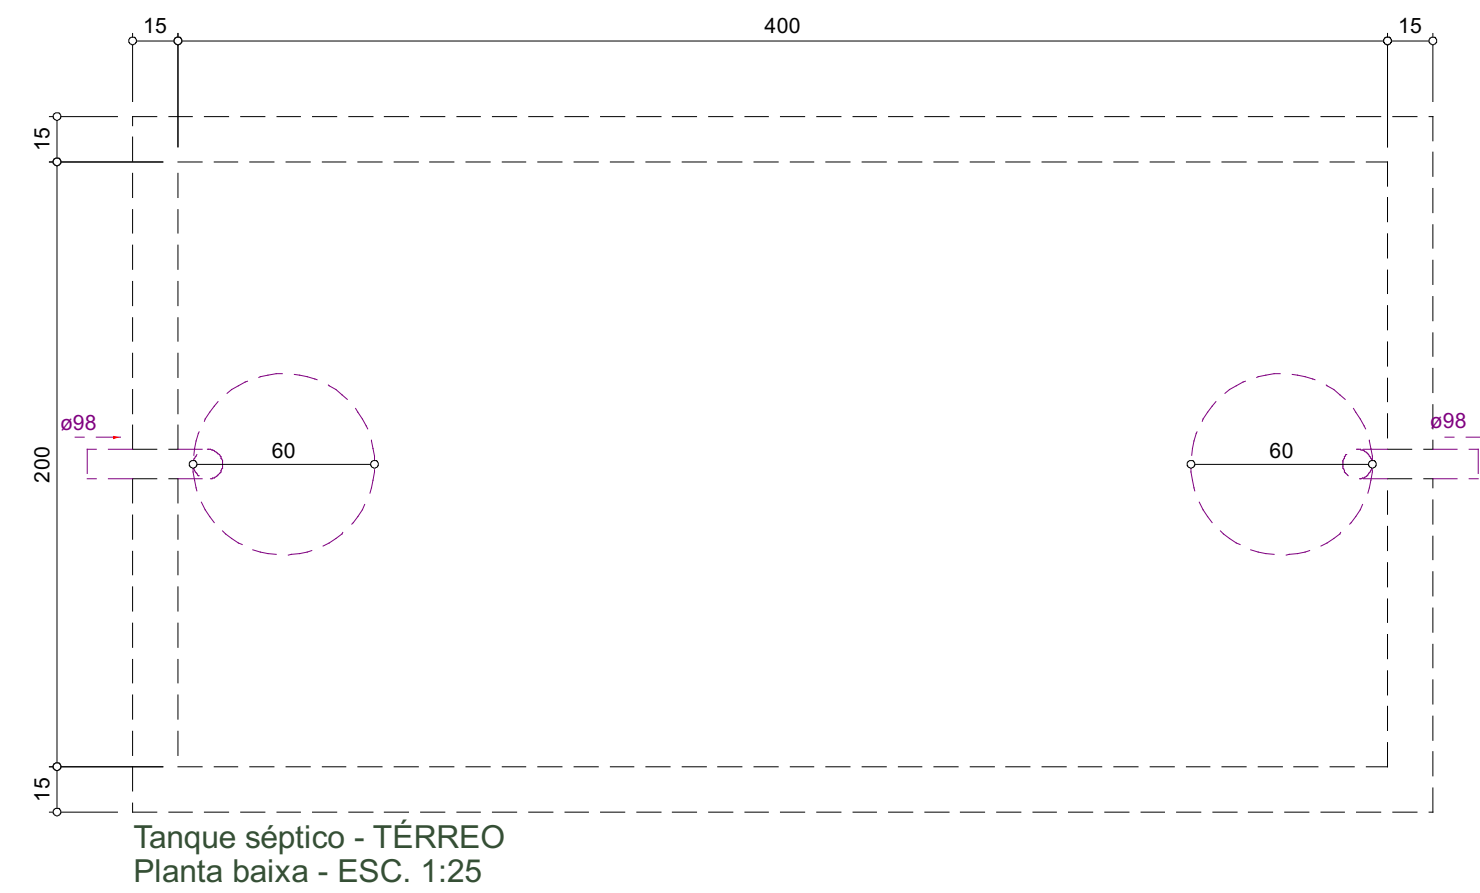

Tanque séptico - TÉRREO
Planta baixa - ESC. 1:25

UFAL

PROJETO SANITÁRIO E PLUVIAL

REVISÃO	DESCRIÇÃO	DATA

CLIENTE				
Anamália Ferreira da Silva				
DESCRIÇÃO DO PROJETO / ENDEREÇO				
PROJETO IHS				
CONTEÚDO DESTA FRONTEIRA				
DETALHES, CORTES E LEGENDAS				
ESCALA	DATA	ÁREA DO TERRENO	ÁREA CONSTRUÍDA	ÁREA DA COBERTA
INDICADA	03/06/2026	1269,00m²	2820,00m²	375m²

RESPONSÁVEL PELO PROJETO				
Autor do projeto: DANIELLY SETTON, GABRIEL BRAGA, PEDRO GABRIEL LEONARDO RAMIRES, PEDRO VICTOR, ROBERTO VINÍCIUS				
CONTRATANTE		RESPONSÁVEL PELA EXECUÇÃO		
CPF:		CREA:		